
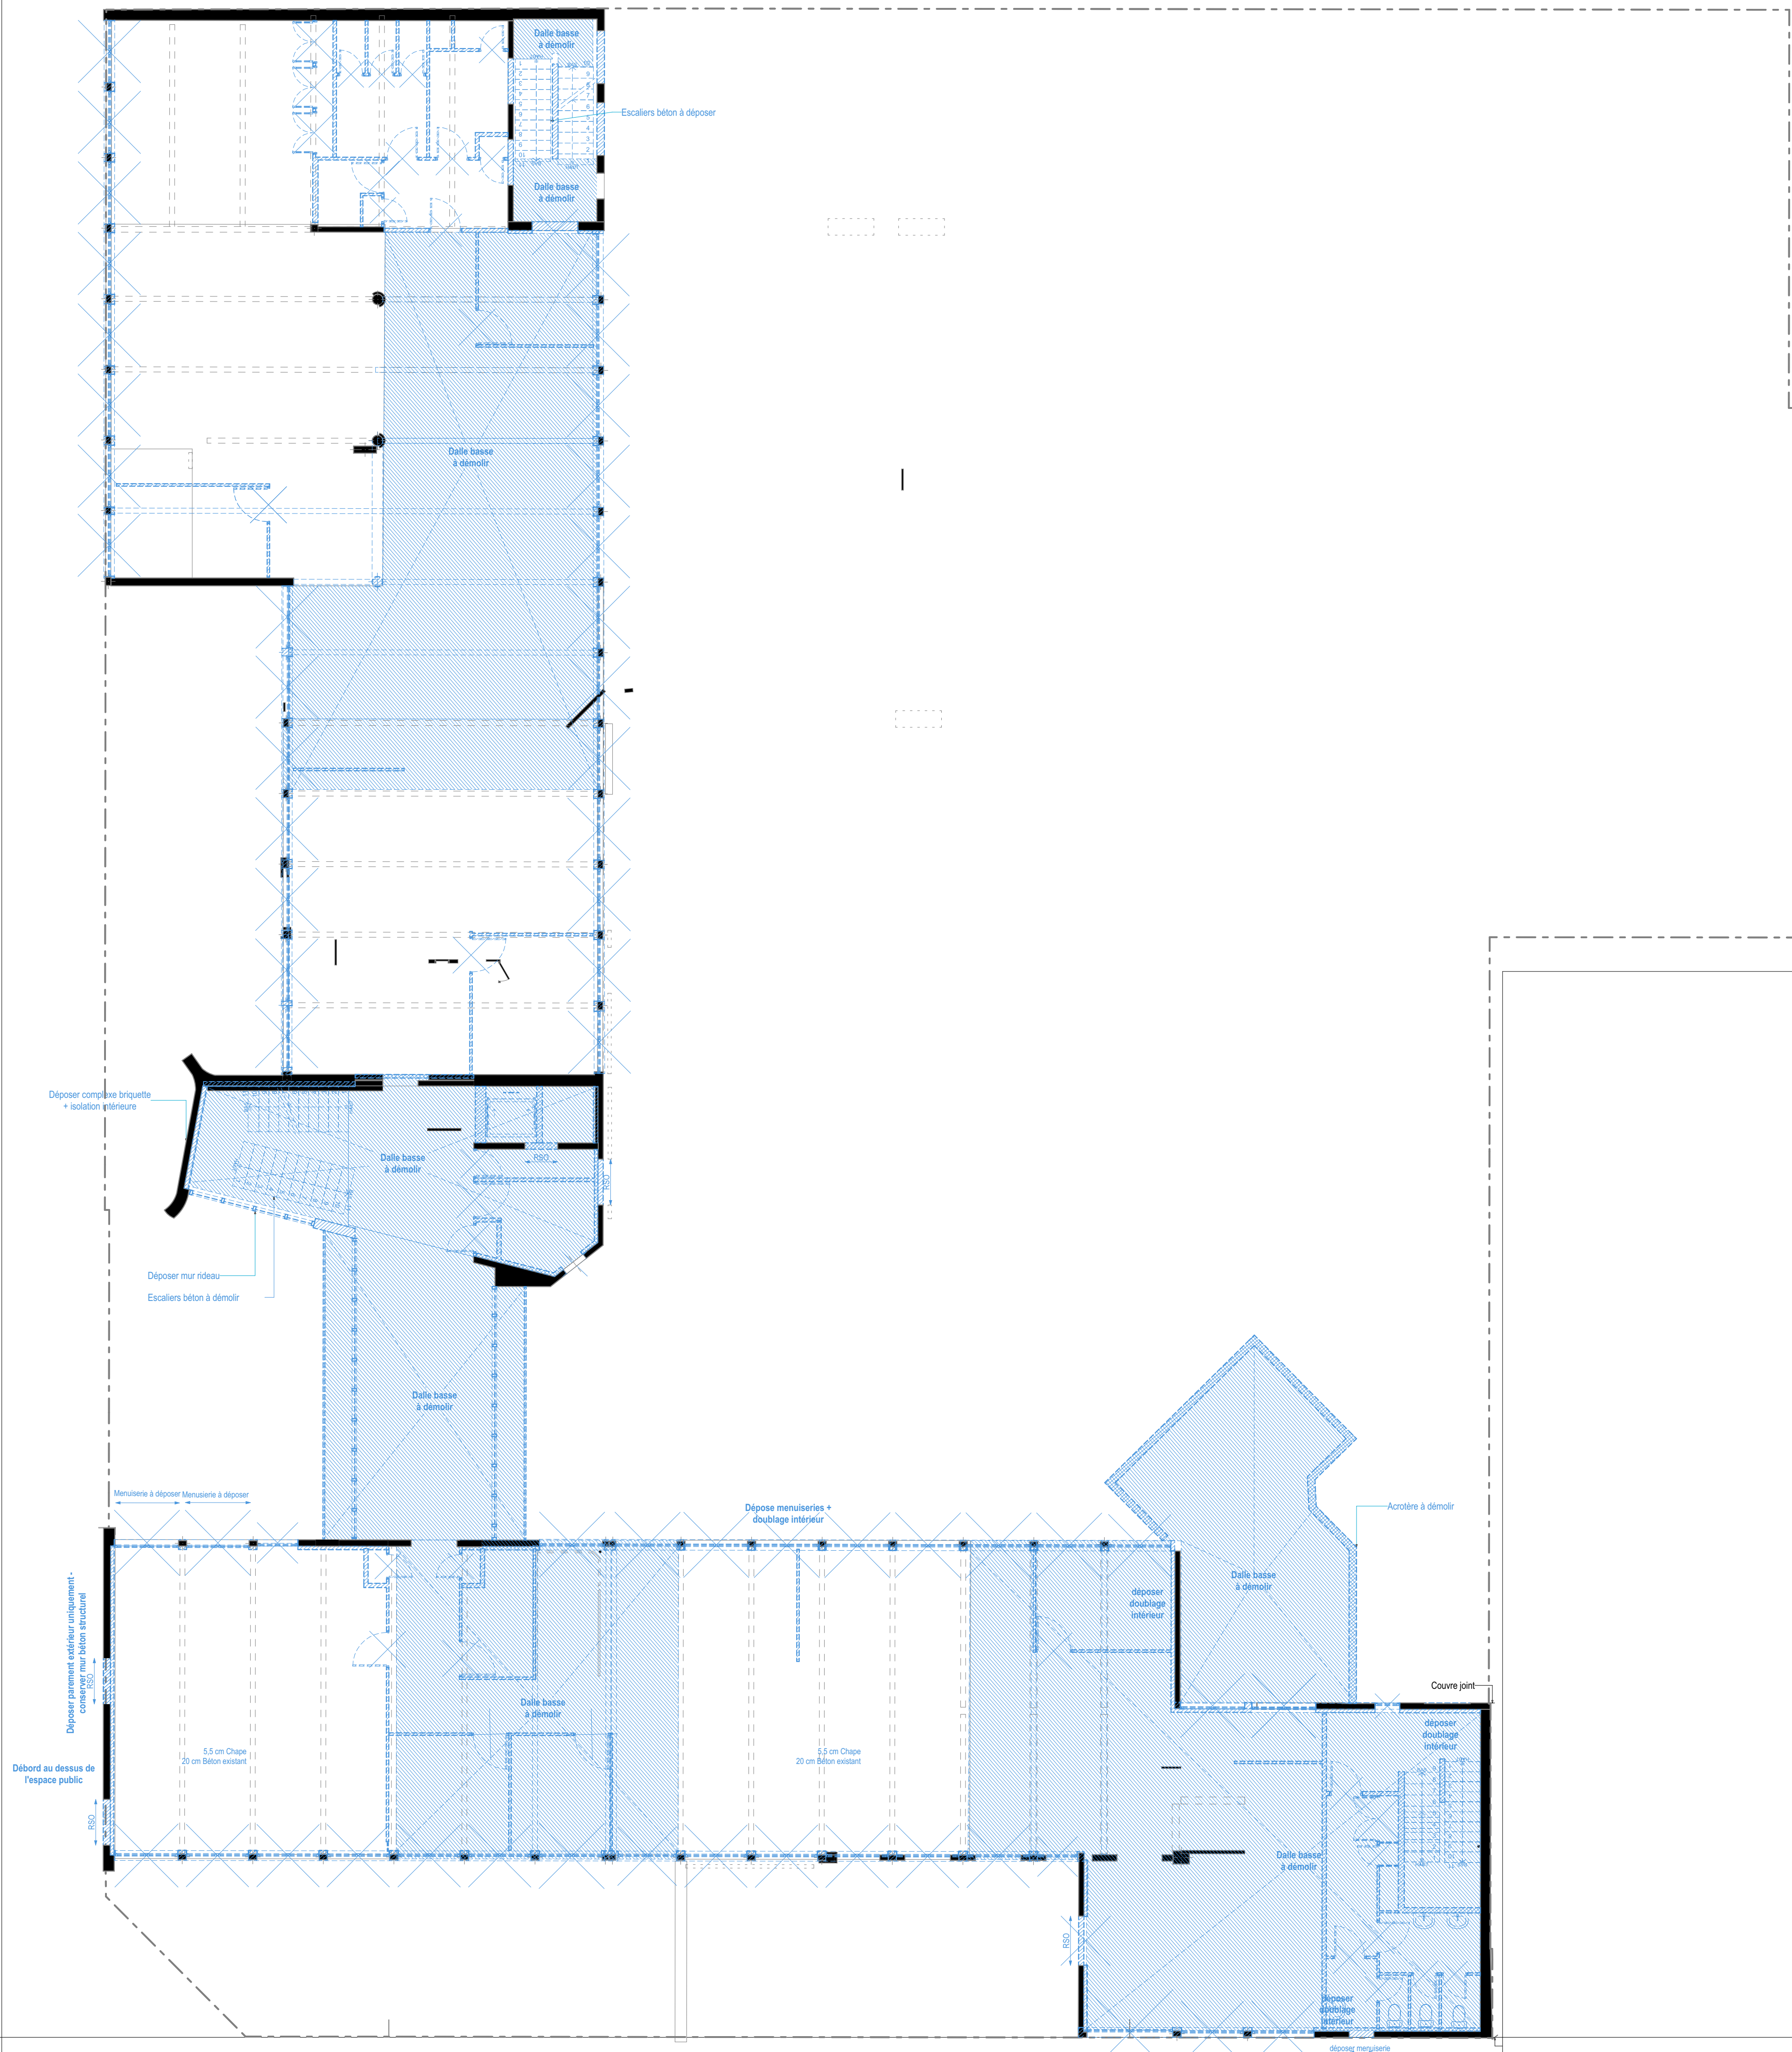


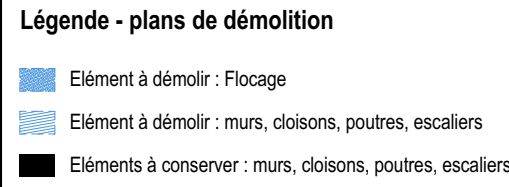

13 CRS DOC JEAN DAMIDOT , 69100 Villeurbanne

Construction d'une résidence sénior et d'un bâtiment tertiaire

Maîtrise d'Ouvrage	SPHE 24 rue Diebold, 69009 Lyon Directeur de programmes : ##### Directeur technique : #####	Tél. 06 74 69 30 07 #### #####
Architecte	EXNDO ARCHITECTURE 3, rue Saint-Martin des Terreaux, 69001 LYON Pierre-Emmanuel Renard	Tél. 04 78 39 44 28 Tél. per@exndo.com
BET Structure	EMBS 17 rue Louis guérin 69100 Villeurbanne Adeline Ledroit	Adeline.embs@ingephil.fr Tél. 06 61 26 68 78
BET Fluides	GC2E 17 rue Louis guérin 69100 Villeurbanne Hervé Seguret	hseguret.gc2e@ingephil.fr Tél. 04 78 16 06 16
Economiste	BET Philippe 17 rue Louis guérin 69100 Villeurbanne Richard Fraisse	Richard.betphilippe@ingephil.fr Tél. 06 86 27 33 72
Paysagiste	Le ciel par dessus le toit 10 Guis Rambaud, 69002 Lyon Estelle Bruaux	contact@lecielpardessusletoit.fr Tél. 06 76 81 66 29
BE VRD	#Société BE VRD #Adresse BE VRD #Intervenant BE VERD	#Mail BE VRD Tél. #téléphone BE VRD
Bureau de contrôle	APAVE 4 chem Ruisseau, 69130 Ecully Alexandre Raginel	Alexandre.raginel@apave.com Tél. 06 13 57 54 86
SPS	#Société SPS #Adresse SPS #Intervenant SPS	#Mail SPS Tél. #téléphone SPS

plan/n°	indice	Titre	Phase
PRO-01.4.3		R+1	PRO
Format : A0 (texte manuel)		Echelle	14/06/2024

[illegible]