


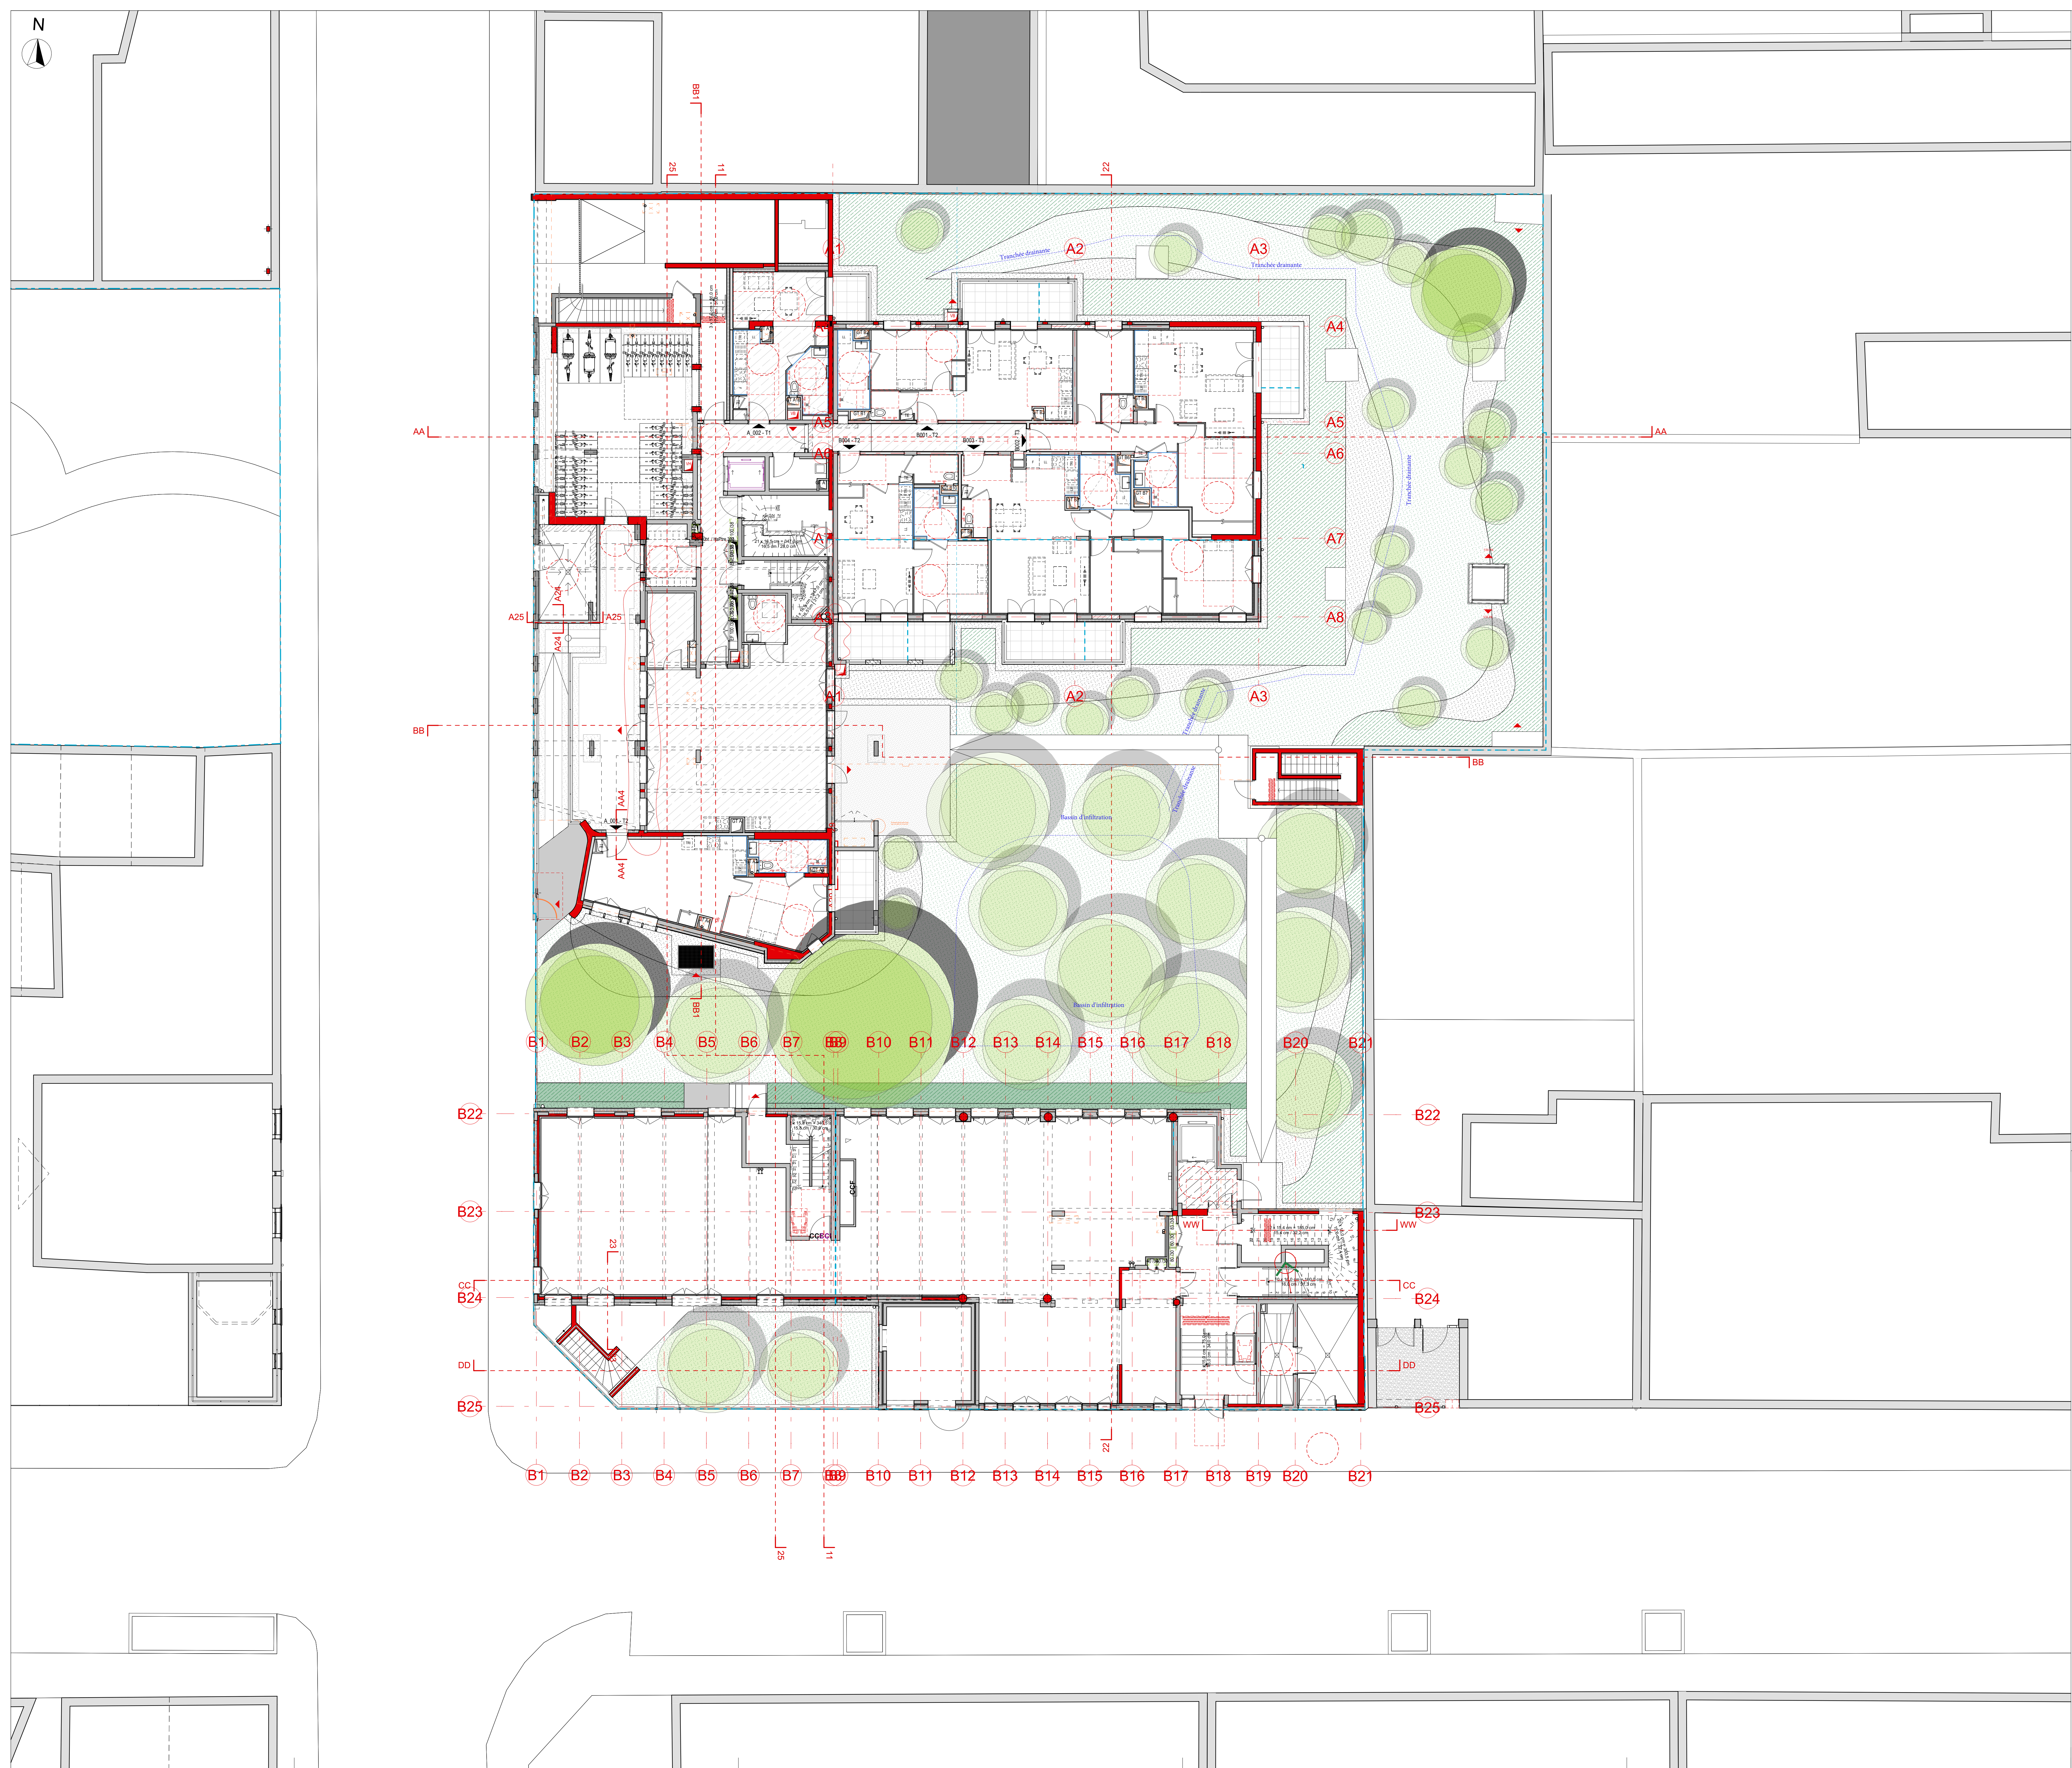

720 / Papillon		
13 CRS DOC JEAN DAMIDOT , 69100 Villeurbanne		
Construction d'une résidence sénior et d'un bâtiment fertilaire		
Maîtrise d'Ouvrage	SPHE 24 rue Desbols, 69009 Lyon Directeur de programmes : **** Directeur technique : ****	Tél. 06 74 69 30 07 **** ****
Architecte	EXNDO ARCHITECTURE 3 rue Saint-Martin des Ternes, 69021 LYON Pierre-Emmanuel Renard	Tél. 04 78 39 44 28 Tél. per@exndo.com
BET Structure	EMBS 17 rue Louis guérin 69100 Villeurbanne Adeline Leduc	Adeline.emb@exnph.fr Tél. 06 61 26 68 76
BET Fluides	GC2E 17 rue Louis guérin 69100 Villeurbanne Hervé Seguret	hseguret@gc2eengineering.fr Tél. 04 78 16 06 16
Economiste	BET Philippe 17 rue Louis guérin 69100 Villeurbanne Richard Froisse	Richard.bet@philippeengineering.fr Tél. 06 86 27 33 72
Paysagiste	Le ciel par dessus le toit 13 Quai Fontenay, 69002 Lyon Estelle Buxaux	contact@lecielpardessusletoit.fr Tél. 06 76 81 66 29
BE VRD	Société BE VRD Adresse BE VRD Intervenant BE VRD	Mail BE VRD Tél. Téléphone BE VRD
Bureau de contrôle	APAVE 4 Chemin Rousseau, 69130 Ecullay Alexandre Ragnhäll	Alexandre.ragnh@apave.com Tél. 06 13 07 54 86
SPS	Société SPS Adresse SPS Intervenant SPS	Mail SPS Tél. Téléphone SPS
plan/n°	Indice	Phase
PRO-01.2.7	RDC	PRO
Format A0 (pays-mat)	Echelle	Date 14/06/2024
Index		
Modifications		
Date		